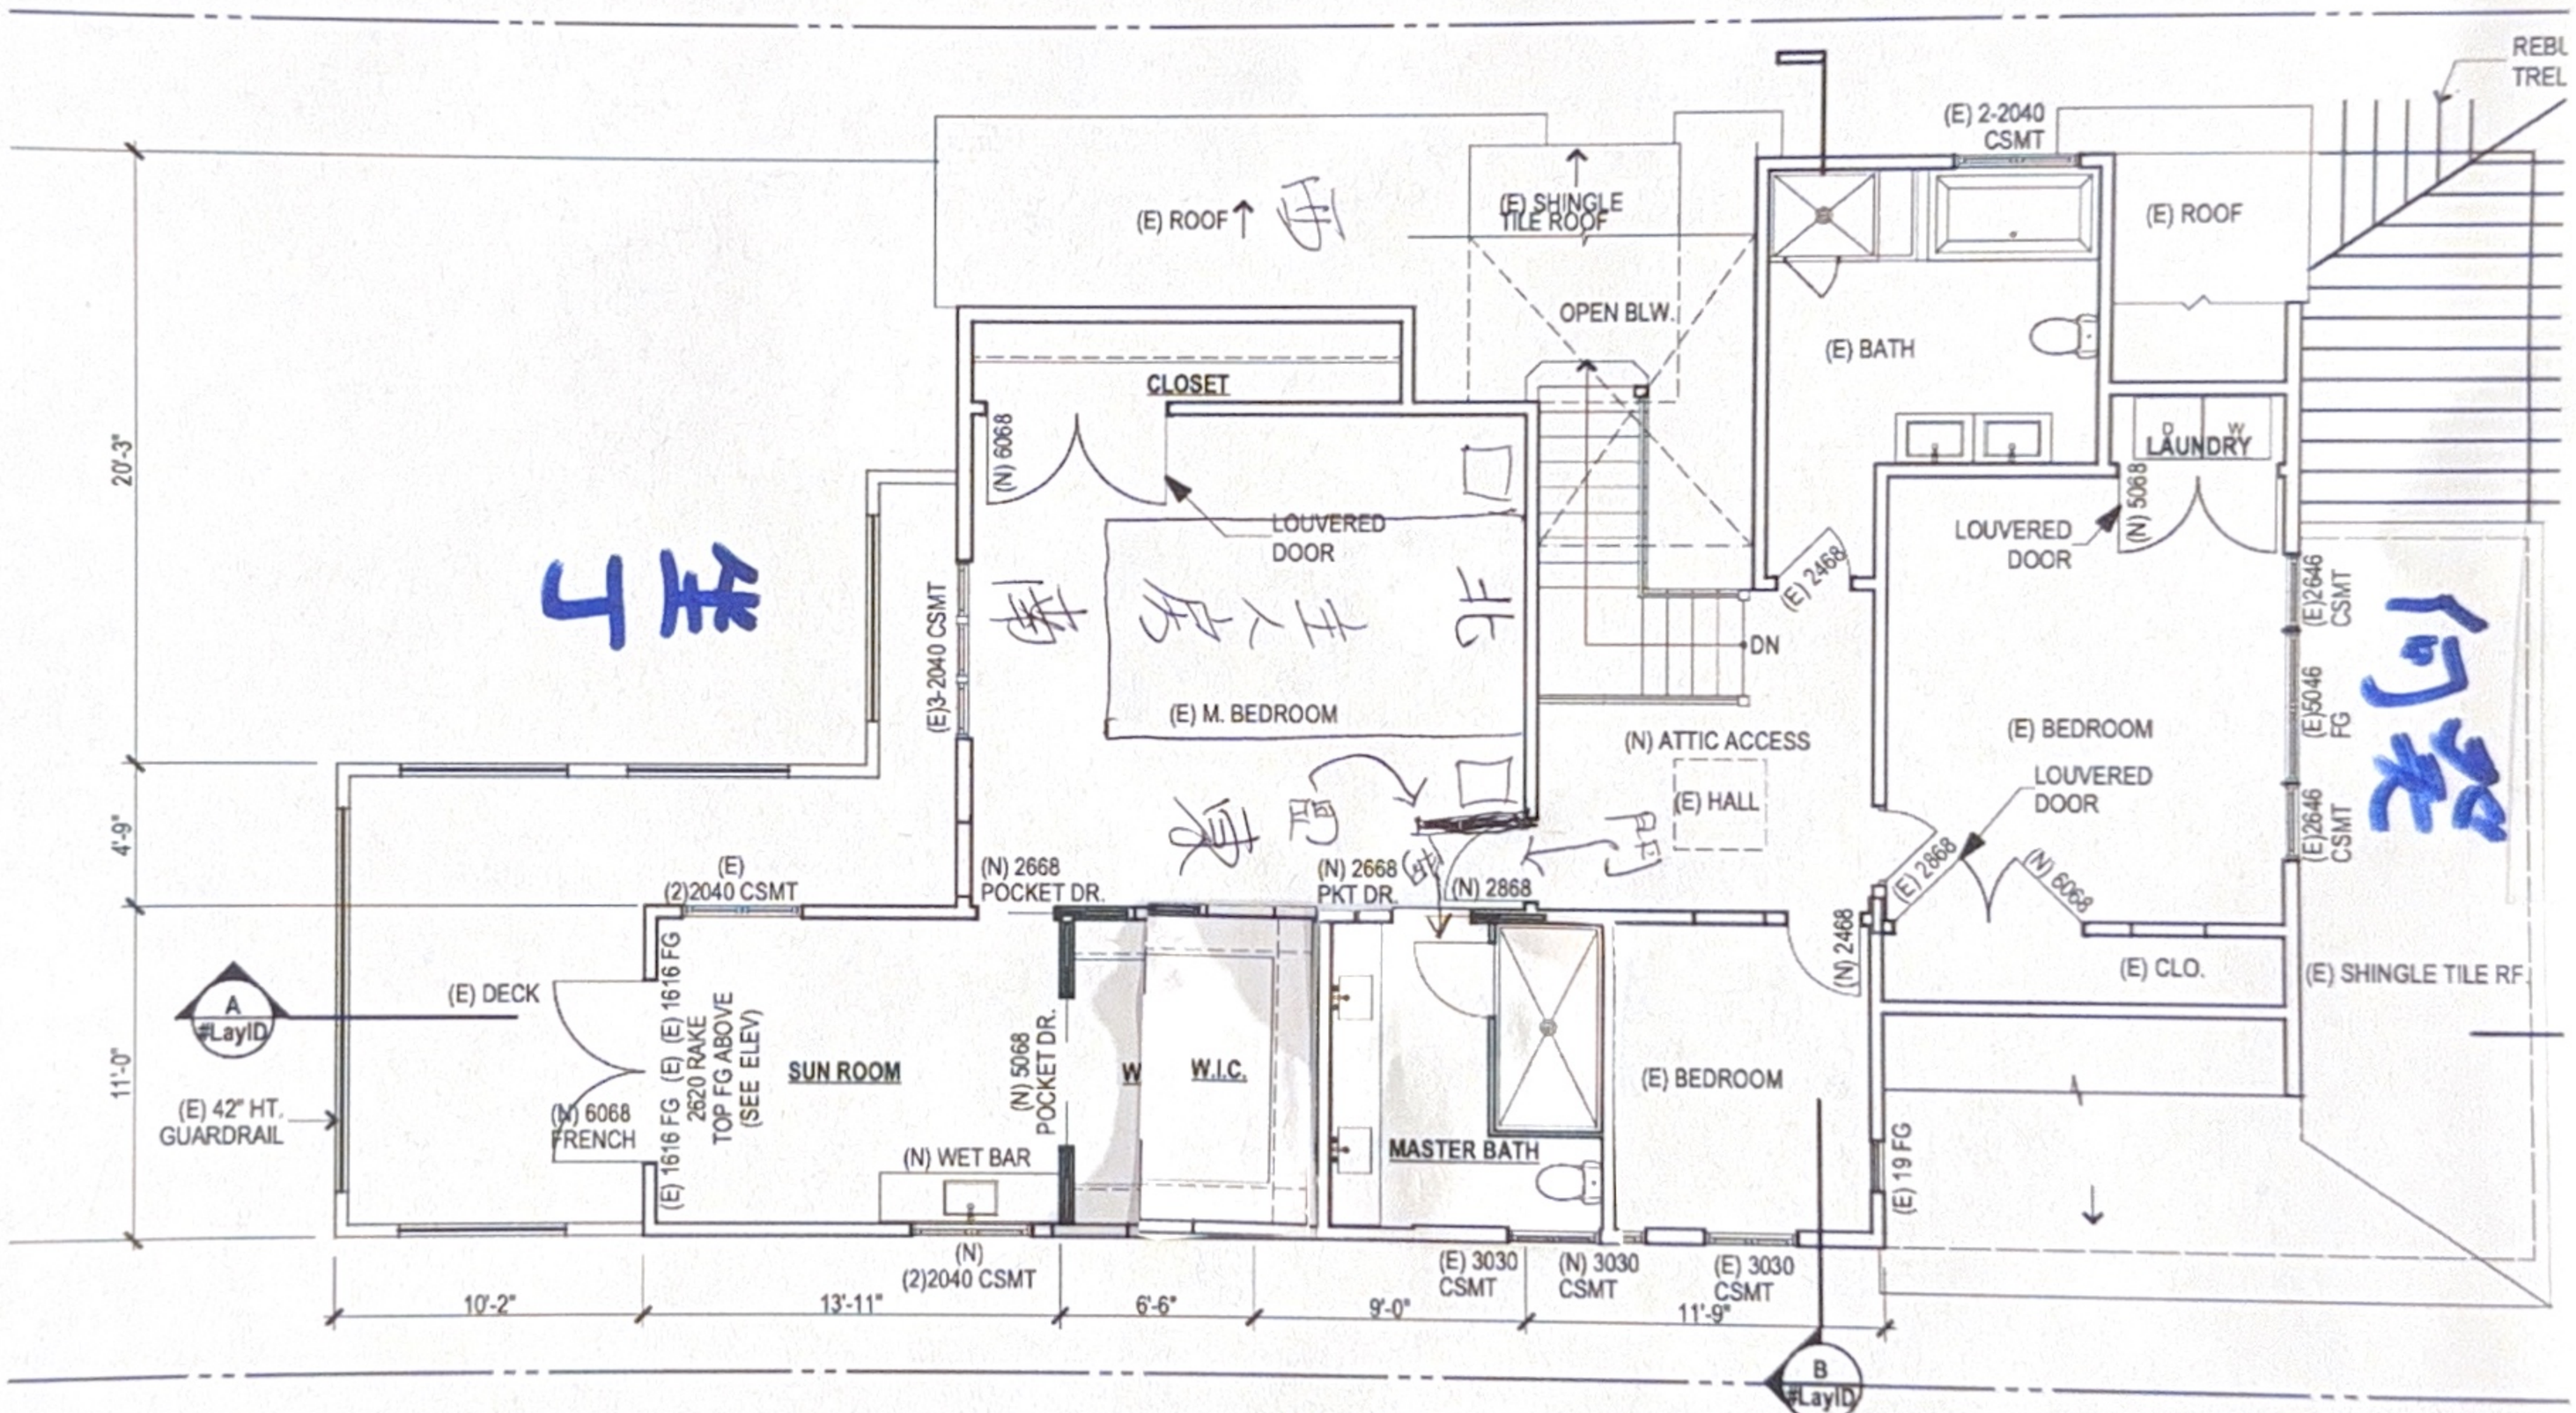
(E) ROOF
(E) SHINGLE TILE ROOF
OPEN BLW.
(E) 2-2040 CSMT
(E) ROOF
REBU TREL
(E) BATH
CLOSET
(N) 6068
LOUVERED DOOR
LAUNDRY
D
W
(N) 5068
LOUVERED DOOR
(E) 2468
DN
(E)3-2040 CSMT
(E) M. BEDROOM
(N) ATTIC ACCESS
(E) HALL
(E) BEDROOM
LOUVERED DOOR
(E)5046 FG
(E)2646 CSMT
(E)2646 CSMT
(E) 2868
(N) 6068
(E) CLO.
(E) SHINGLE TILE RF
(E) (2)2040 CSMT
(N) 2668 POCKET DR.
(N) 2668 PKT DR.
(N) 2868
(N) 2468
(E) DECK
A #LayID
(E) 42" HT. GUARDRAIL
(N) 6068 FRENCH
(E) 1616 FG
(E) 1616 FG
(E) 2620 RAKE TOP FG ABOVE (SEE ELEV)
SUN ROOM
(N) 5068 POCKET DR.
W
W.I.C.
MASTER BATH
(E) BEDROOM
(E) 19 FG
(N) WET BAR
(N) (2)2040 CSMT
(E) 3030 CSMT
(N) 3030 CSMT
(E) 3030 CSMT
B #LayID
20'-3"
4'-9"
11'-0"
10'-2"
13'-11"
6'-6"
9'-0"
11'-9"